POVO 2 — FLOOR REGISTRATION REVIEW

All panels use the same axes and scale; existing geometry, not relocated rooms

Floor -2 — current source slice, z=-3.2 m

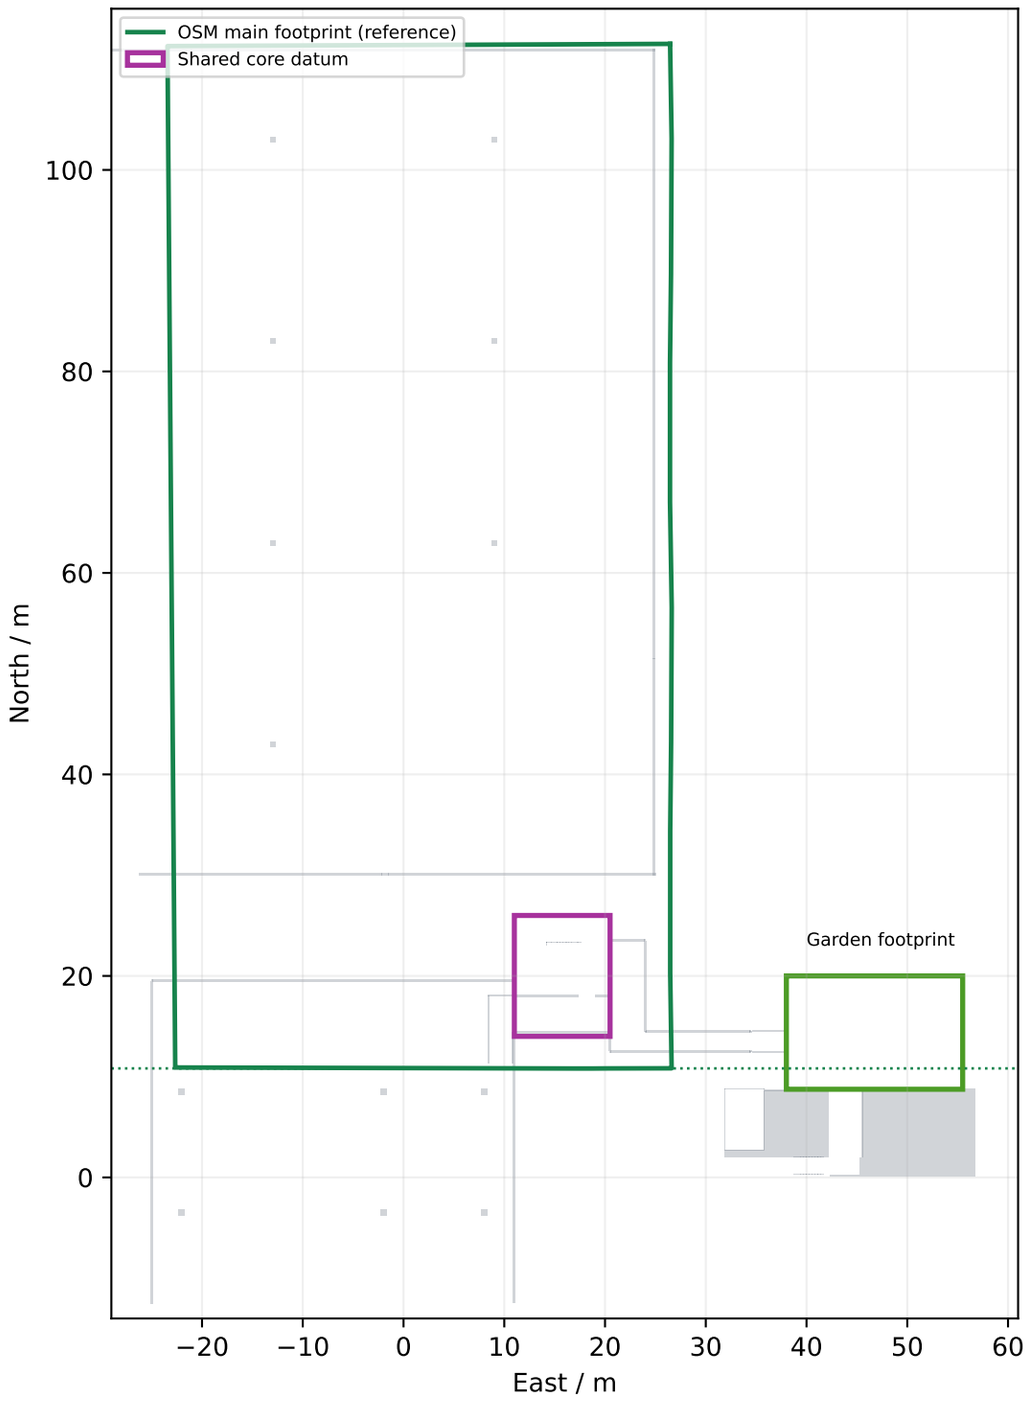

Floor -1 — current source slice, z=0.4 m

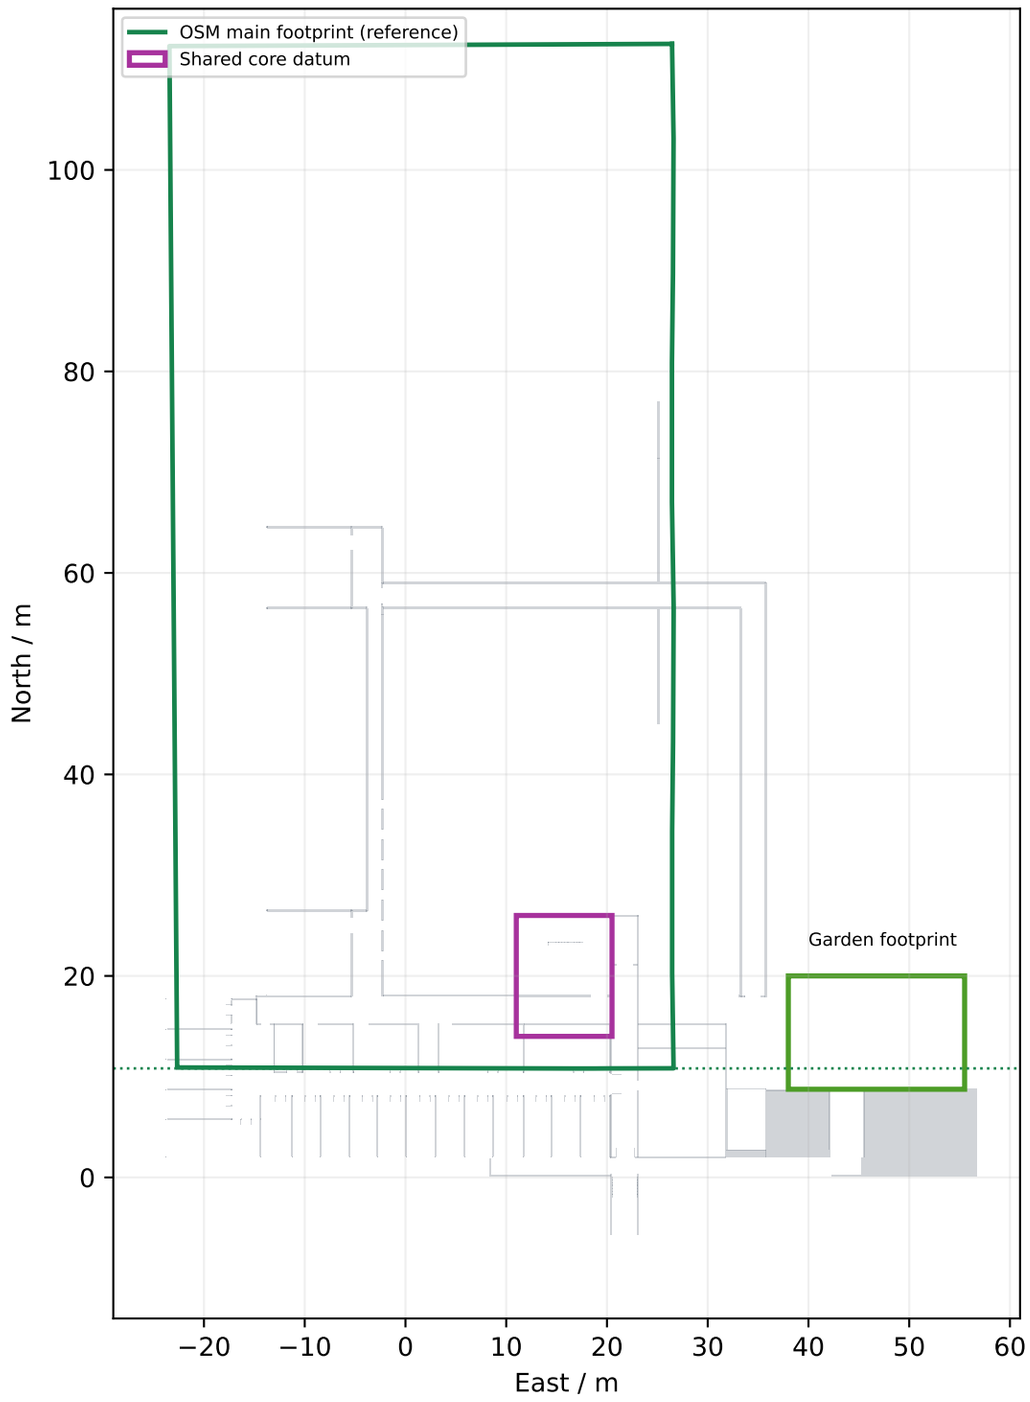

Floor +0 — current source slice, z=4 m

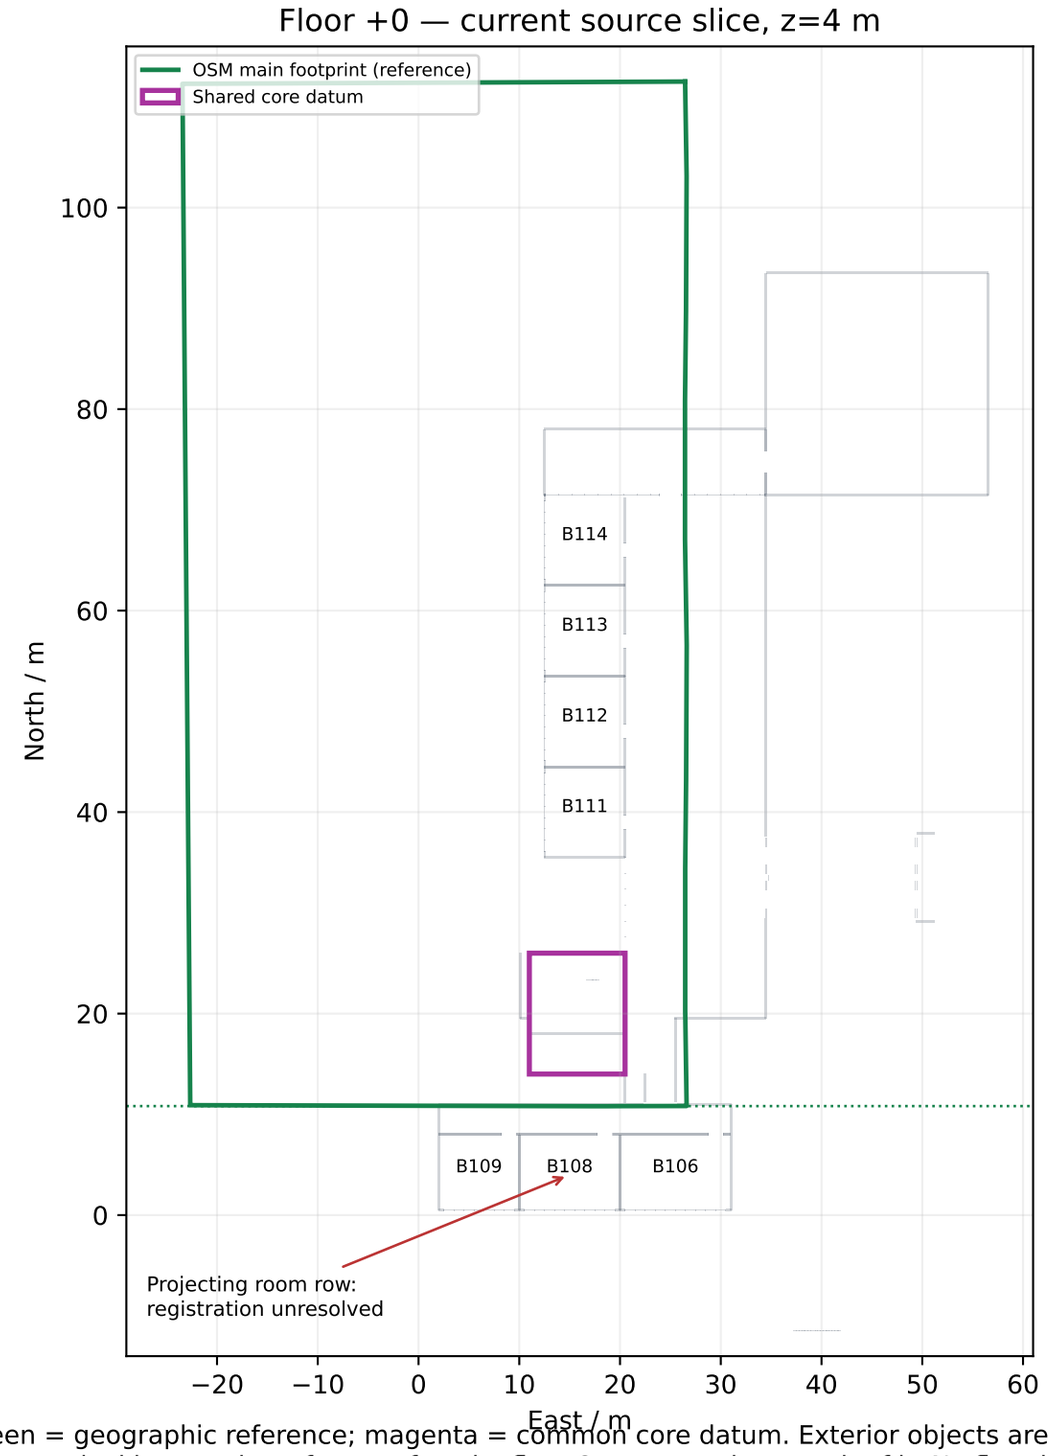

Floor +1 — current source slice, z=11.2 m

Green = geographic reference; magenta = common core datum. Exterior objects are included in the slices.
Upper arrival is near the reference facade; floor-0 rooms project south of it. No floor has been scaled or moved.
Existing floor elevations are source assumptions, not a measured vertical survey.