IMPLEMENTED EXTERIOR CONNECTION — interior layout retained

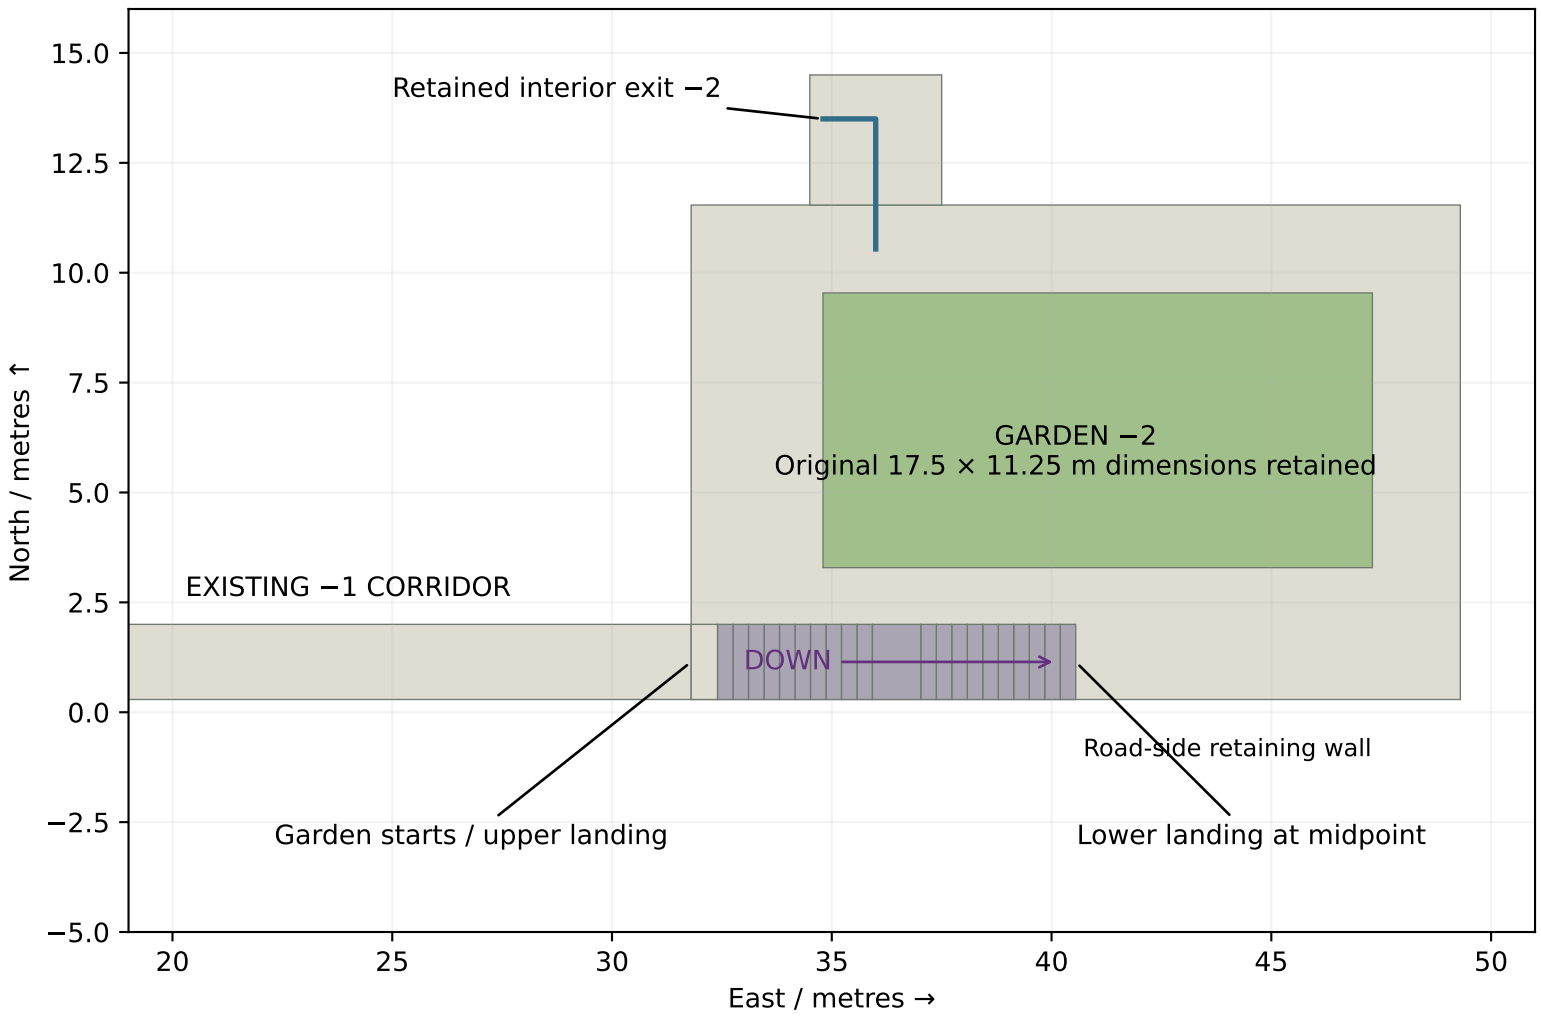

Side elevation — stair descends into garden, not toward road

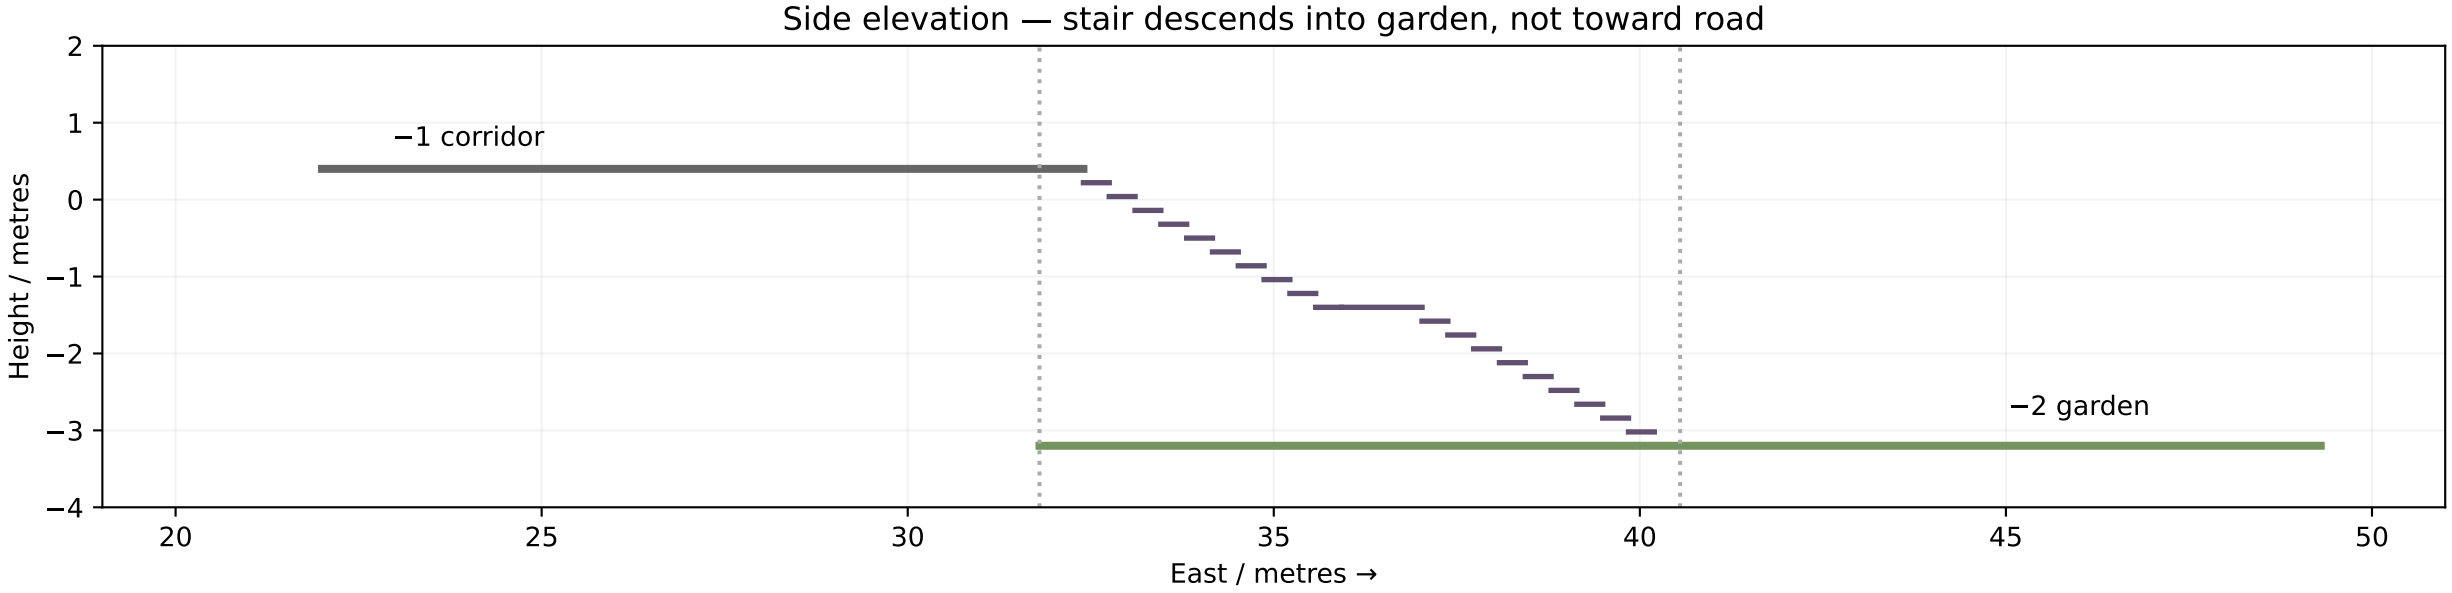

Corridor-anchored source geometry, not surveyed registration. Room/facade and 5 m grass-strip alignment remain pending.