
POVO 2 — ENTRANCE, RECEPTION, STAIR AND CLASSROOM CORRIDORS


Orientation: street entrance at bottom; looking inward. Povo 1 / bridge side is LEFT.

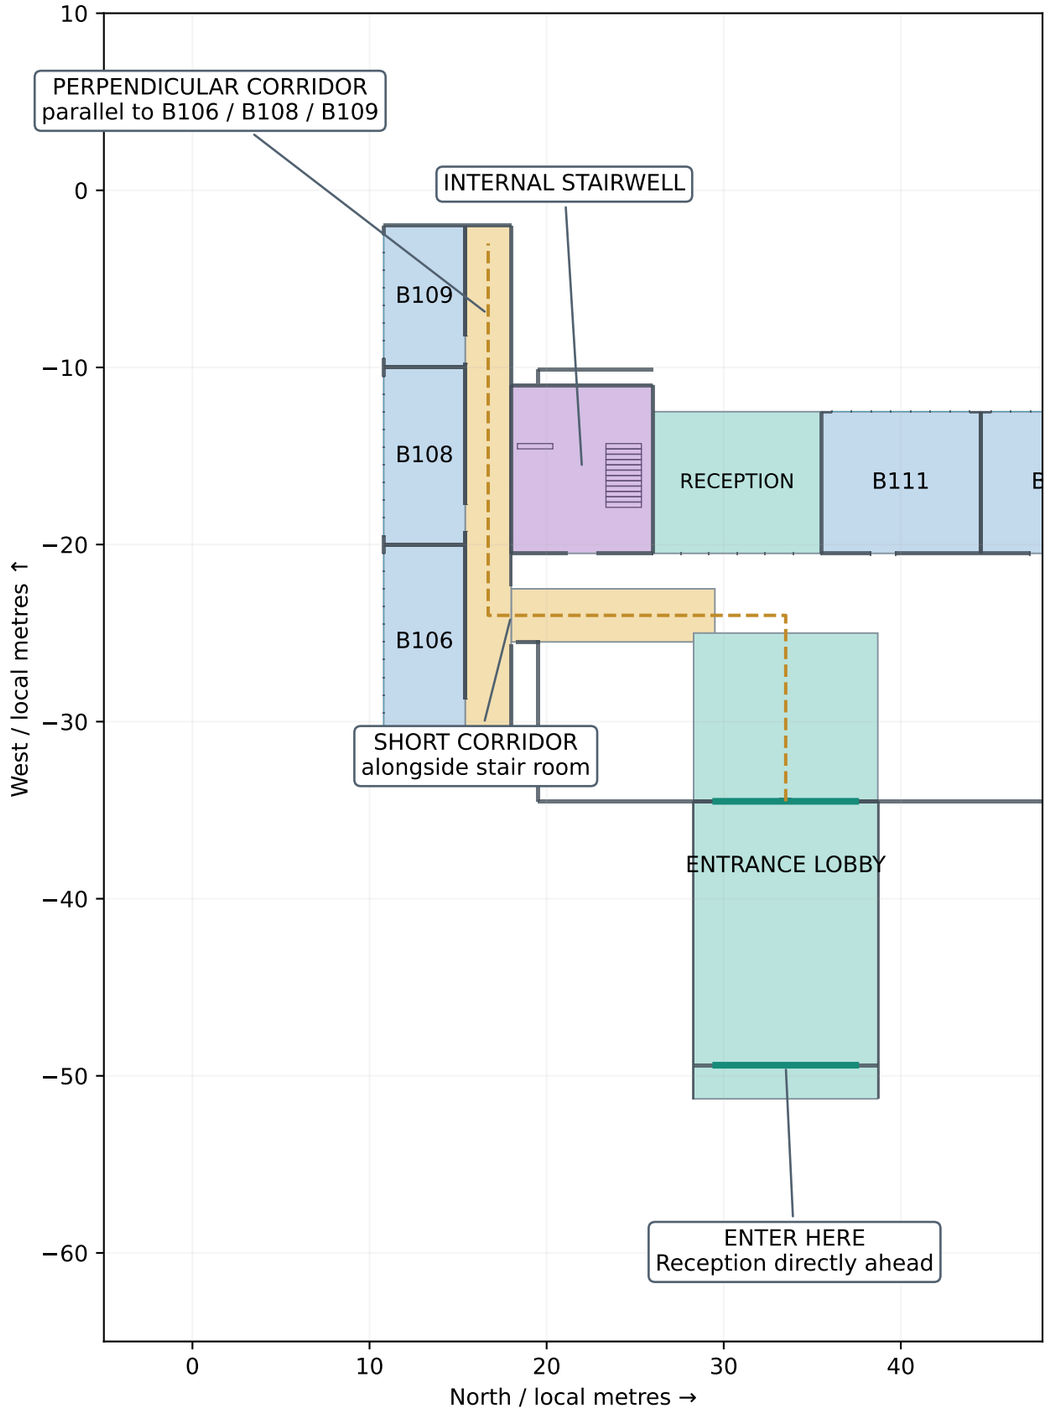

IMPLEMENTED — B106/B108/B109 fit behind the yellow facade; 4.6 m room depth + 2.6 m corridor. Core and basement interiors retained.
Roadside grass registration awaits the basement facade alignment check. The accepted exterior connection is on the final page.

POVO 2 — FLOOR 0 / FULL MODELLED INTERIOR


Orientation: street entrance at bottom; looking inward. Povo 1 / bridge side is LEFT.

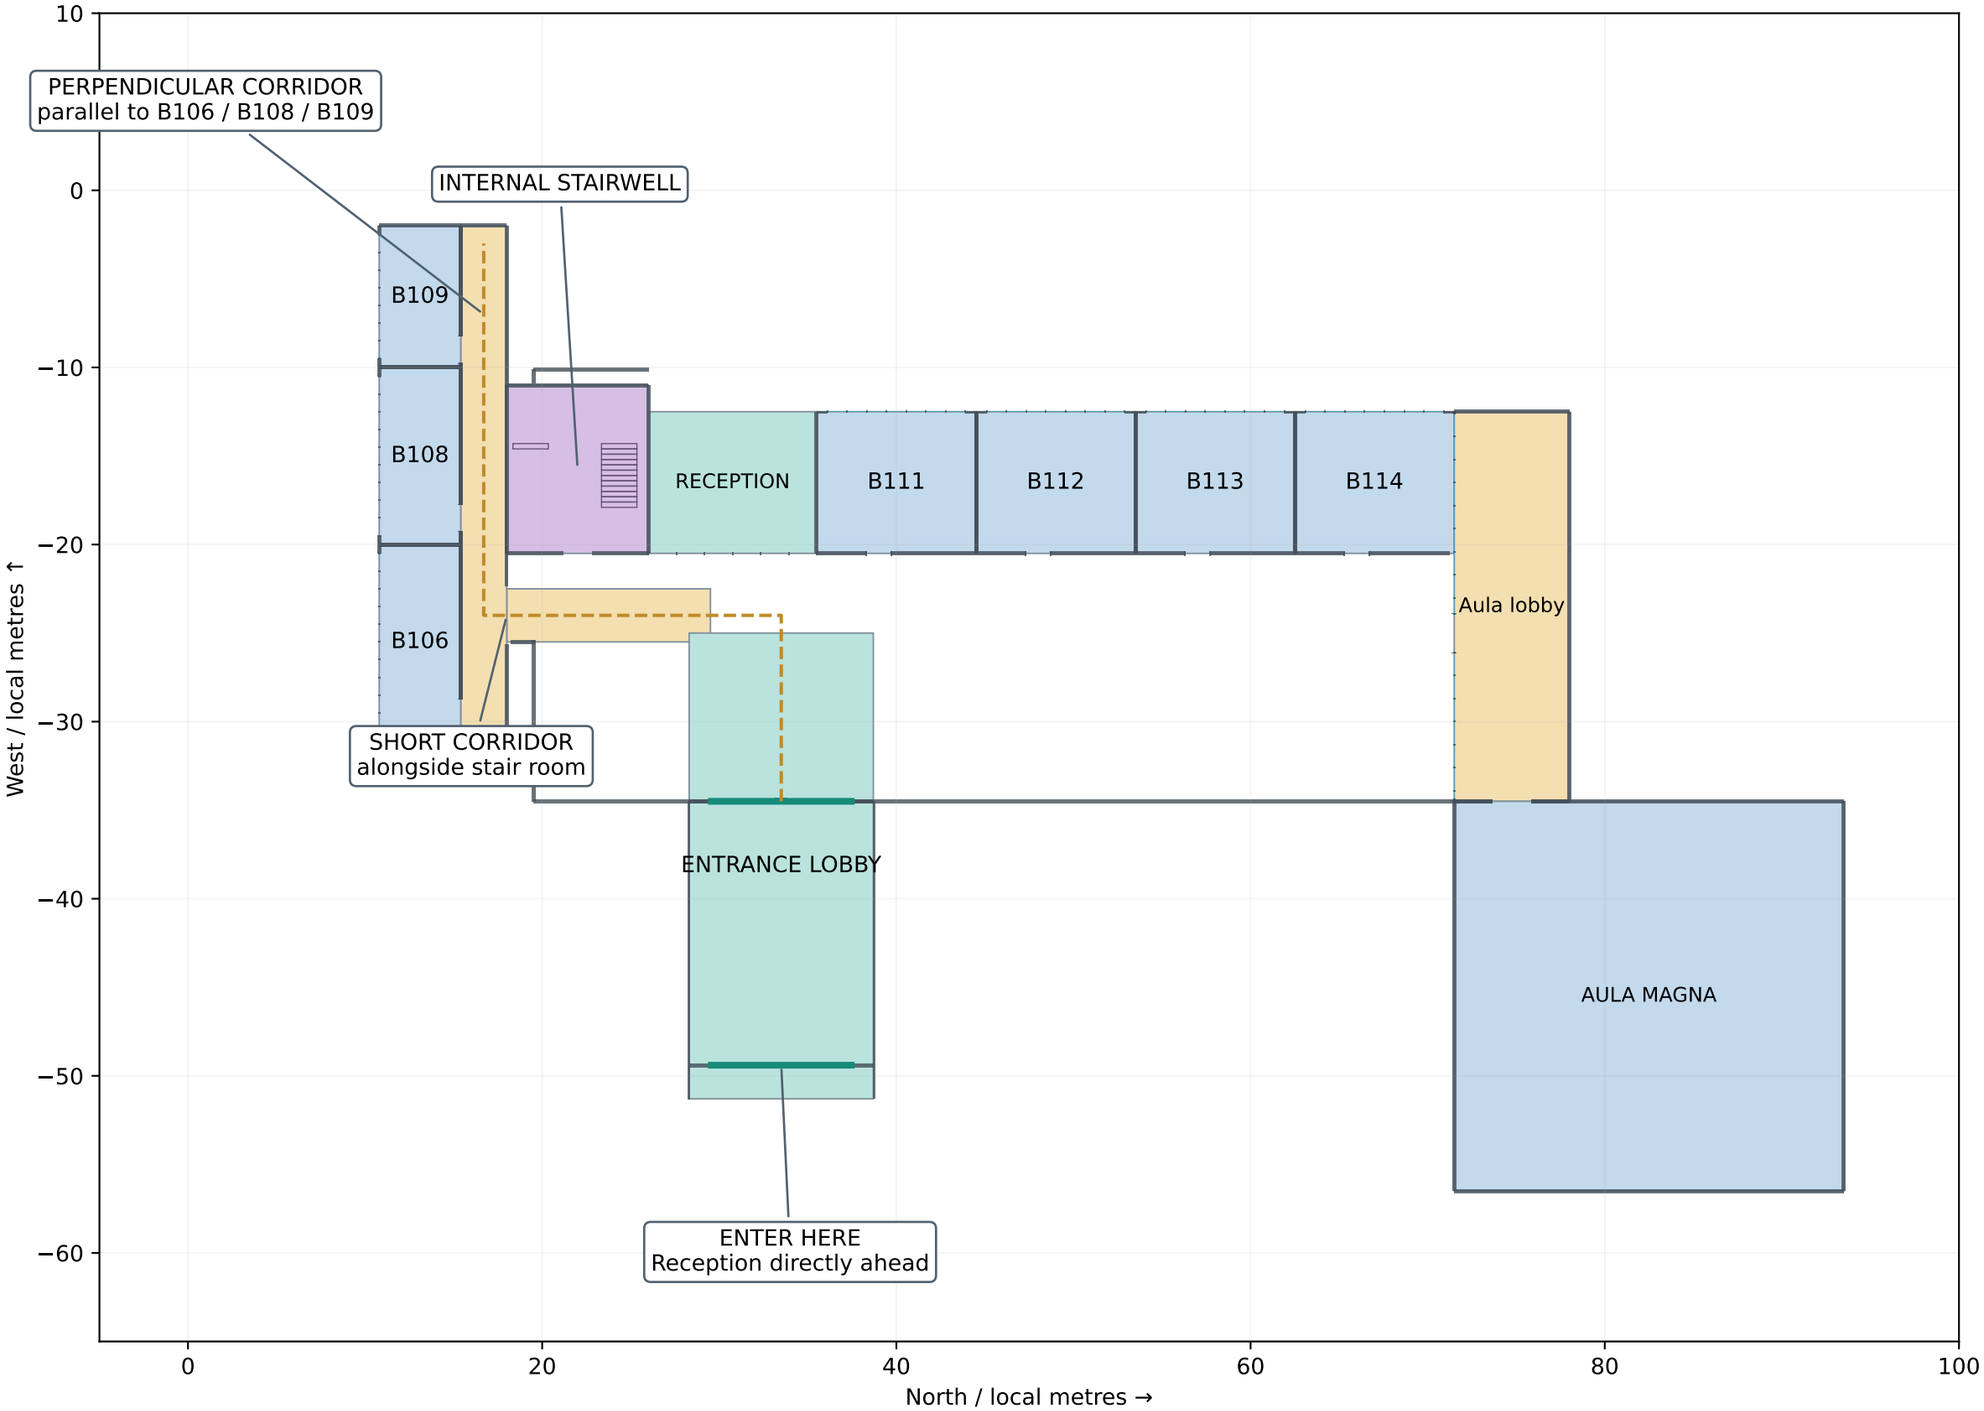

IMPLEMENTED — B106/B108/B109 fit behind the yellow facade; 4.6 m room depth + 2.6 m corridor. Core and basement interiors retained.
Roadside grass registration awaits the basement facade alignment check. The accepted exterior connection is on the final page.

POVO 2 — FLOOR −1 / EXISTING INTERIOR AND EXTERNAL EXIT


Orientation: street entrance at bottom; looking inward. Povo 1 / bridge side is LEFT.

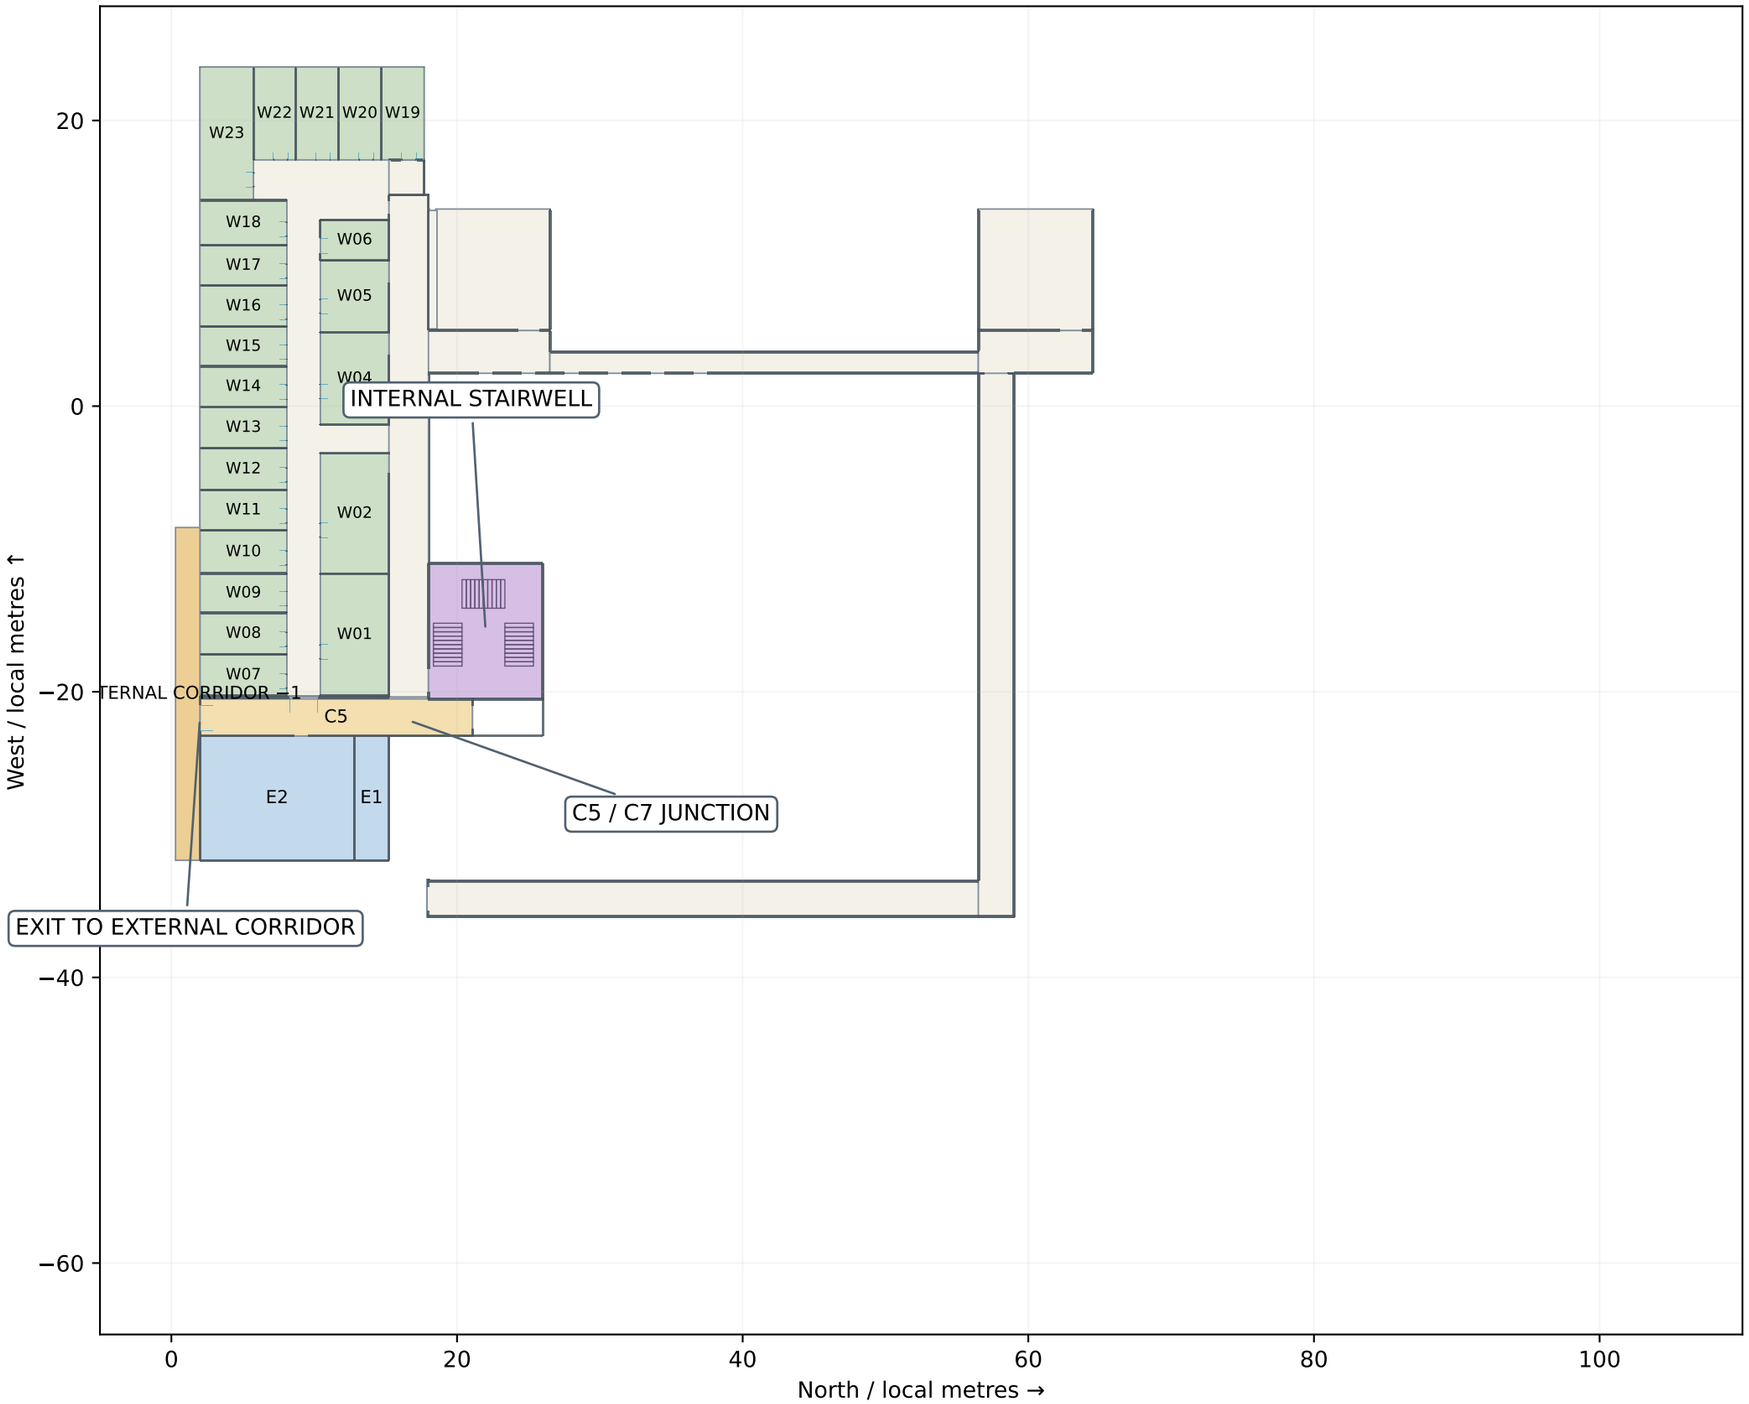

IMPLEMENTED — B106/B108/B109 fit behind the yellow facade; 4.6 m room depth + 2.6 m corridor. Core and basement interiors retained.
Roadside grass registration awaits the basement facade alignment check. The accepted exterior connection is on the final page.

POVO 2 — FLOOR −2 / EXISTING INTERIOR ACCESS


Orientation: street entrance at bottom; looking inward. Povo 1 / bridge side is LEFT.

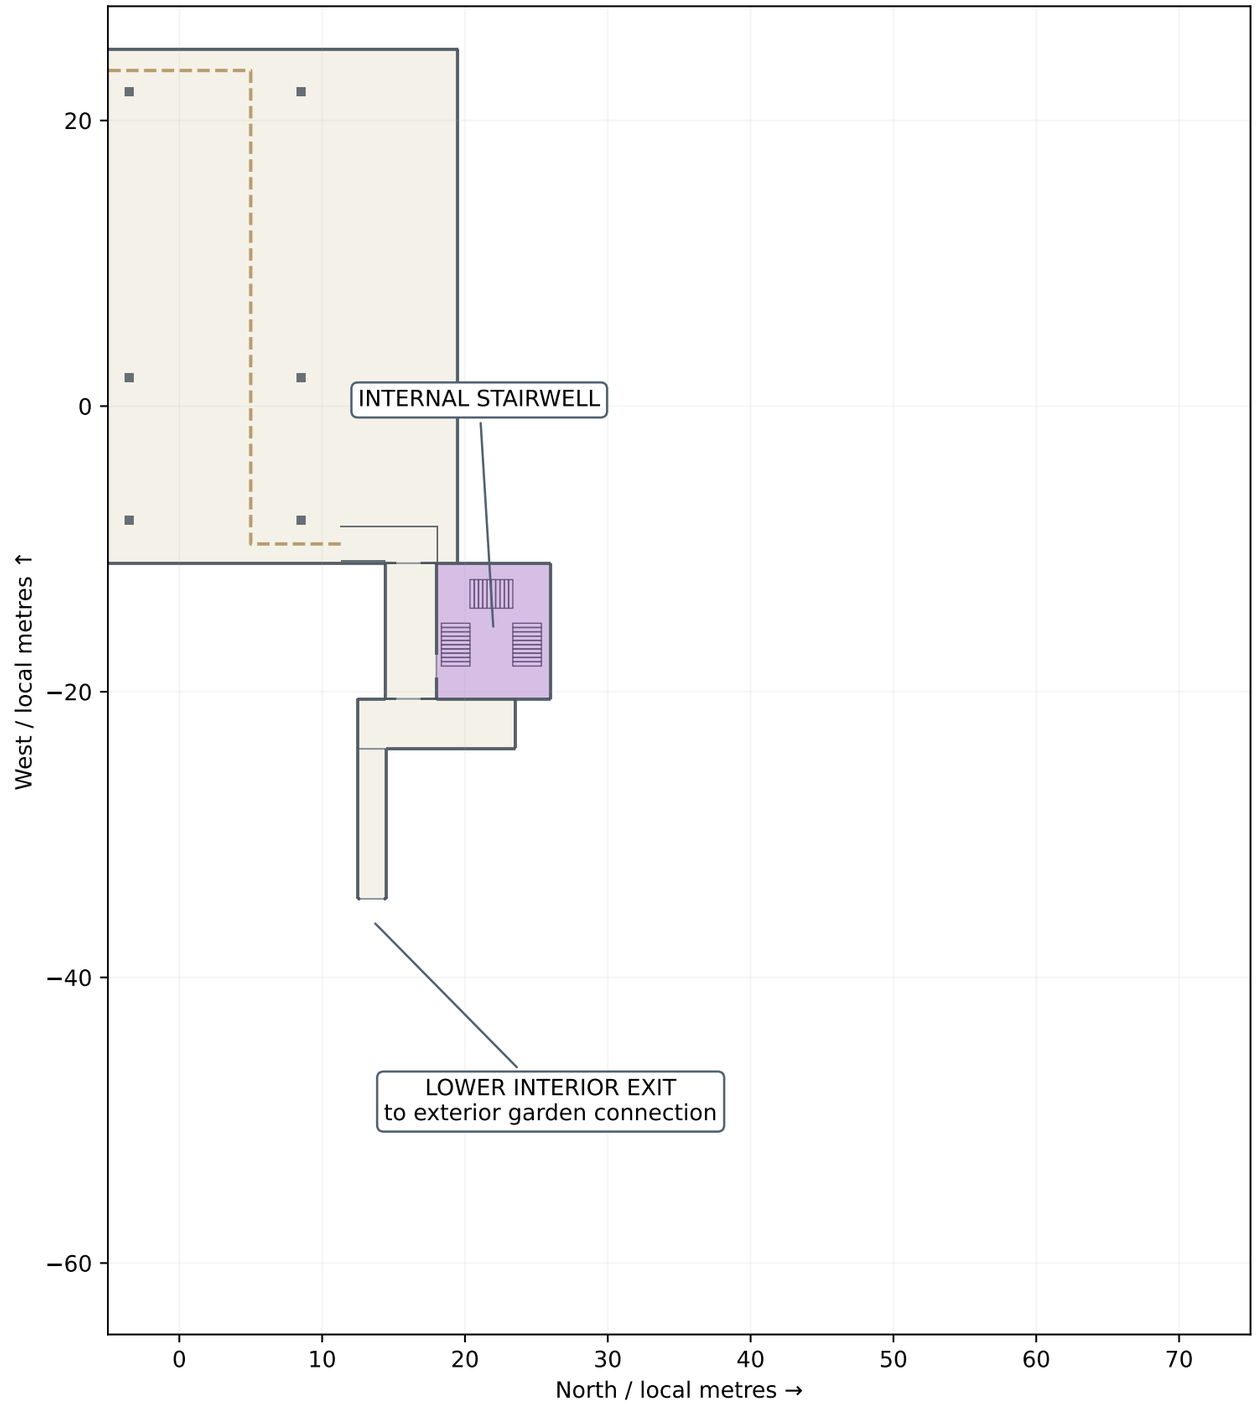

IMPLEMENTED — B106/B108/B109 fit behind the yellow facade; 4.6 m room depth + 2.6 m corridor. Core and basement interiors retained.
Roadside grass registration awaits the basement facade alignment check. The accepted exterior connection is on the final page.

POVO 2 — FLOOR +1 / MODELLED BRIDGE ARRIVAL


Orientation: street entrance at bottom; looking inward. Povo 1 / bridge side is LEFT.

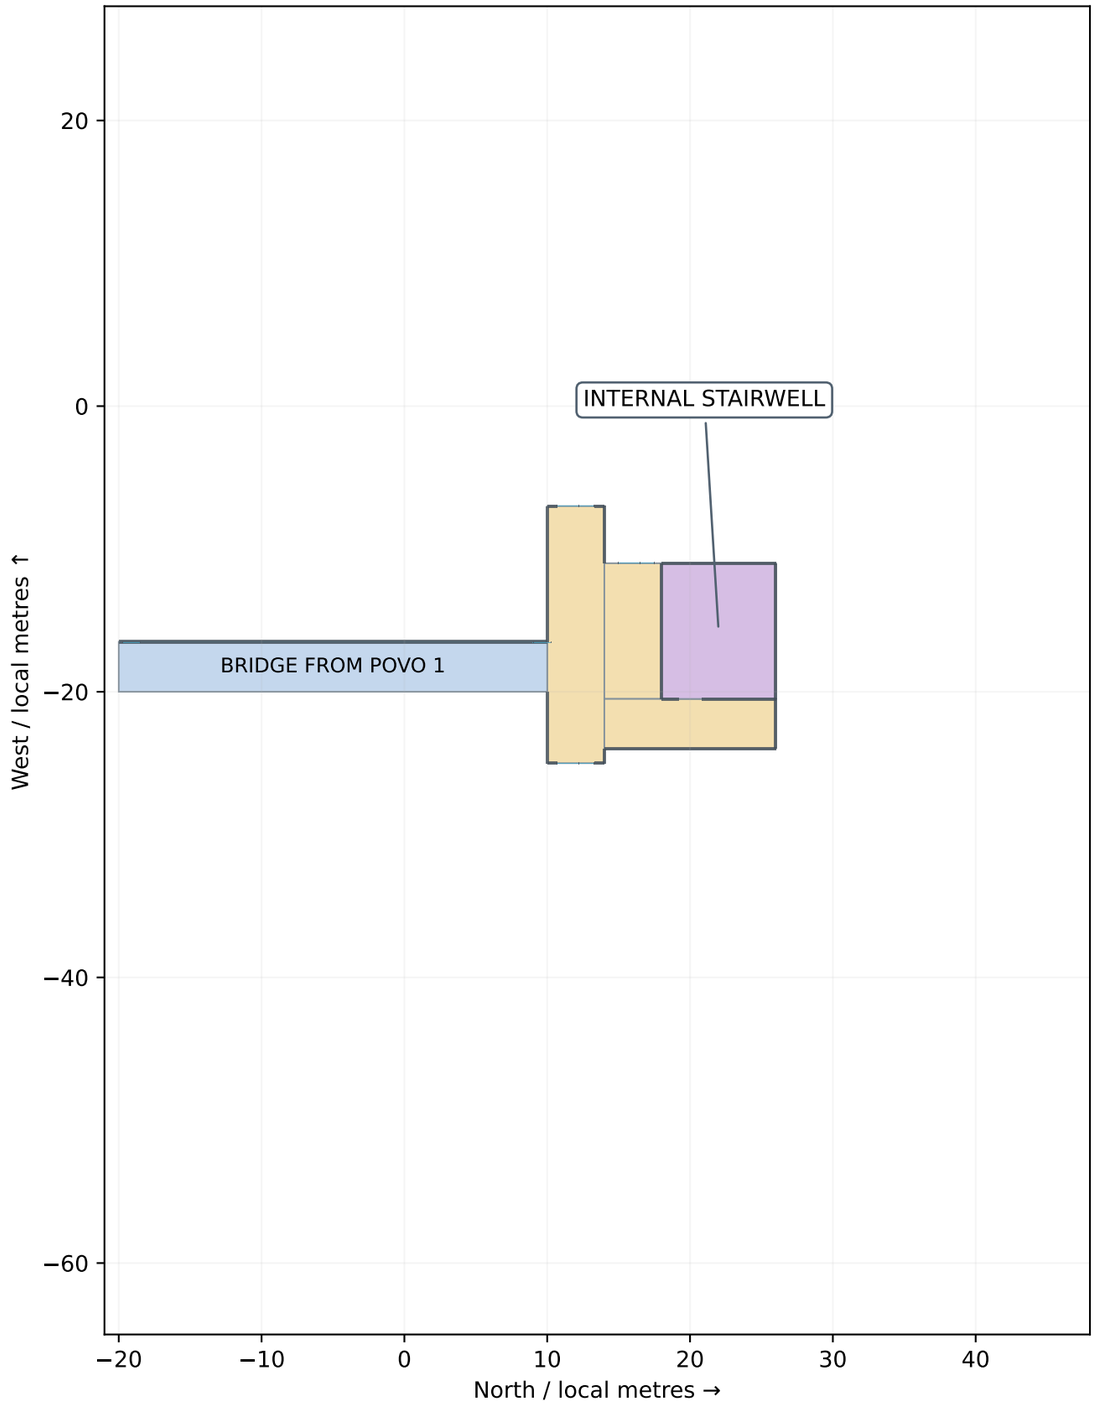

IMPLEMENTED — B106/B108/B109 fit behind the yellow facade; 4.6 m room depth + 2.6 m corridor. Core and basement interiors retained.
Roadside grass registration awaits the basement facade alignment check. The accepted exterior connection is on the final page.

POVO 2 — CORRIDOR, STAIR AND LOWER GARDEN

Corrected connection • schematic, not to scale

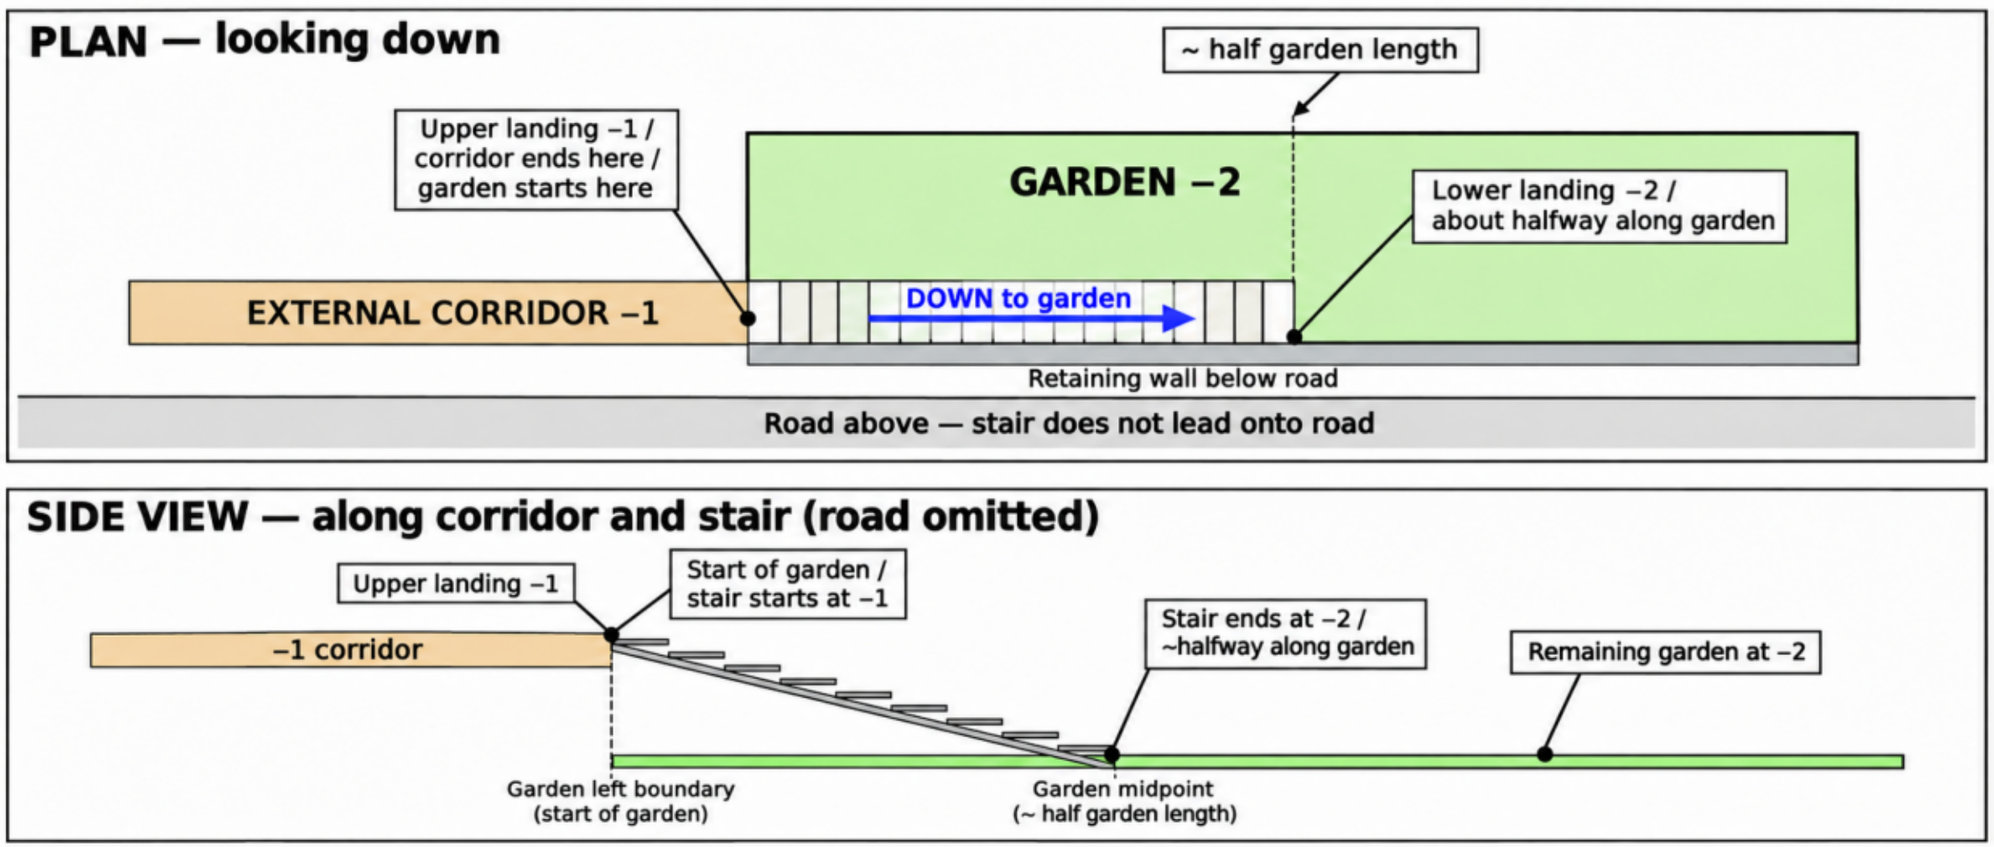

Straight corridor → upper landing at garden edge → descending stair → lower landing near garden midpoint. No interior-layout changes shown.