POVO 2 — FINAL IMPLEMENTED FLOOR REGISTRATION

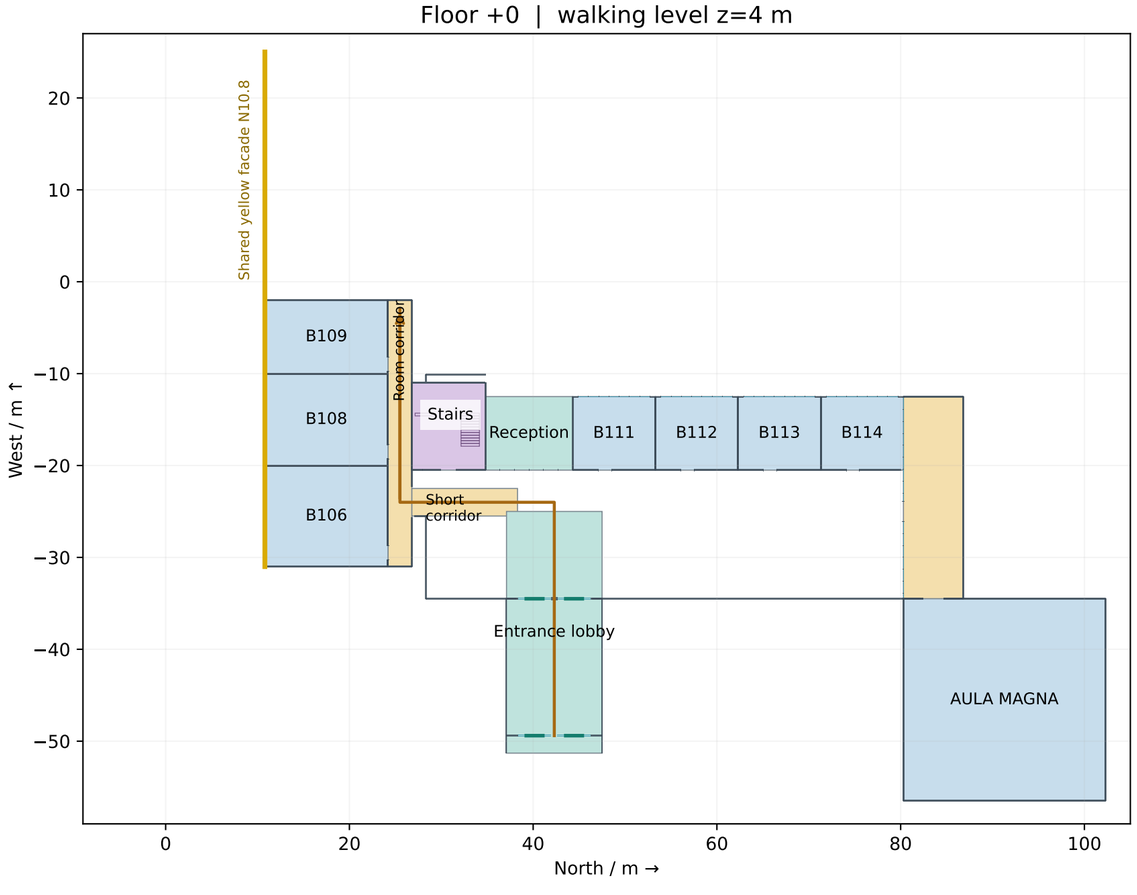

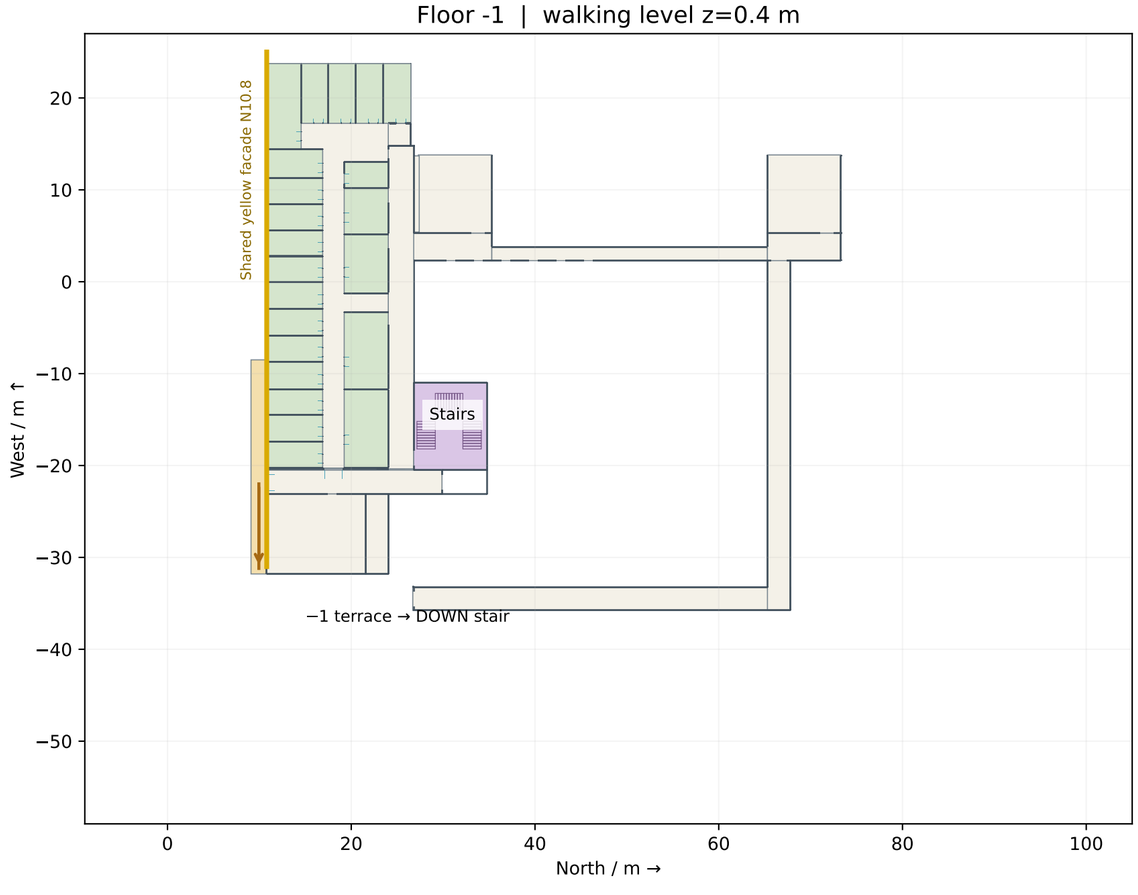

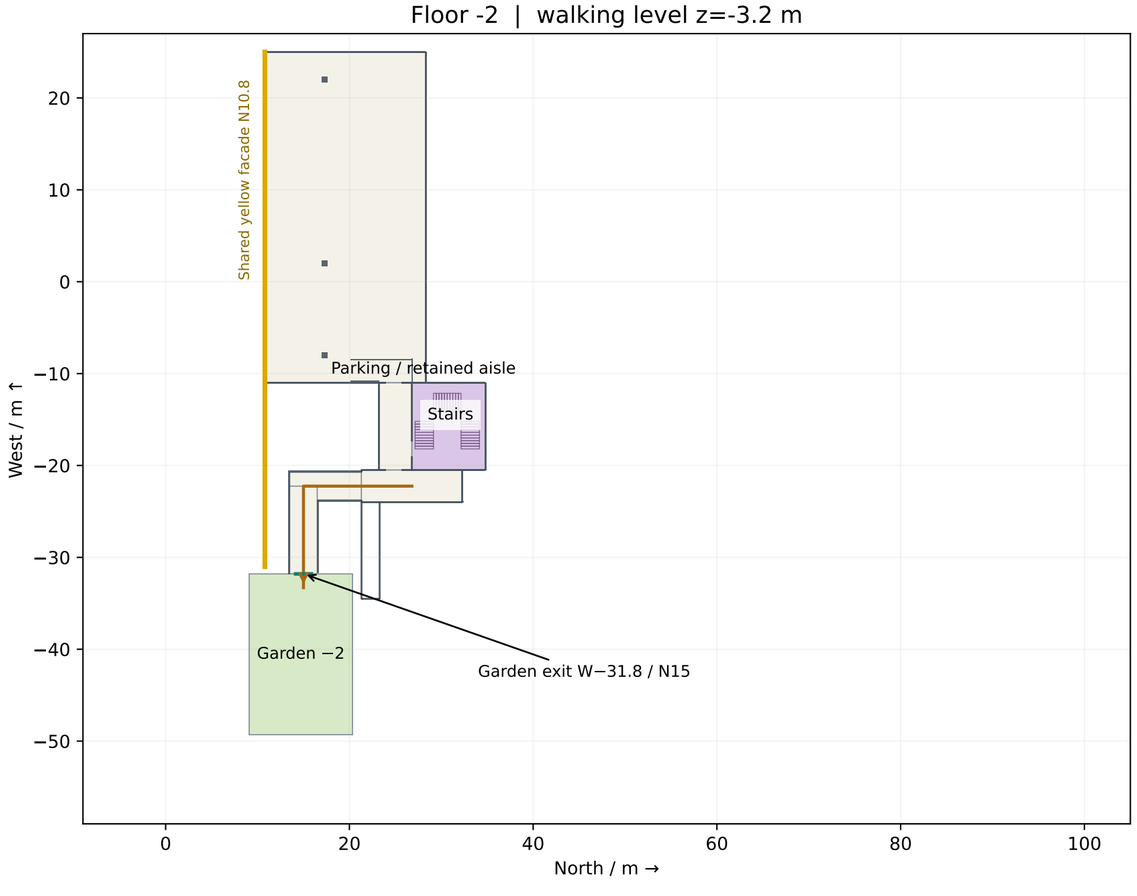

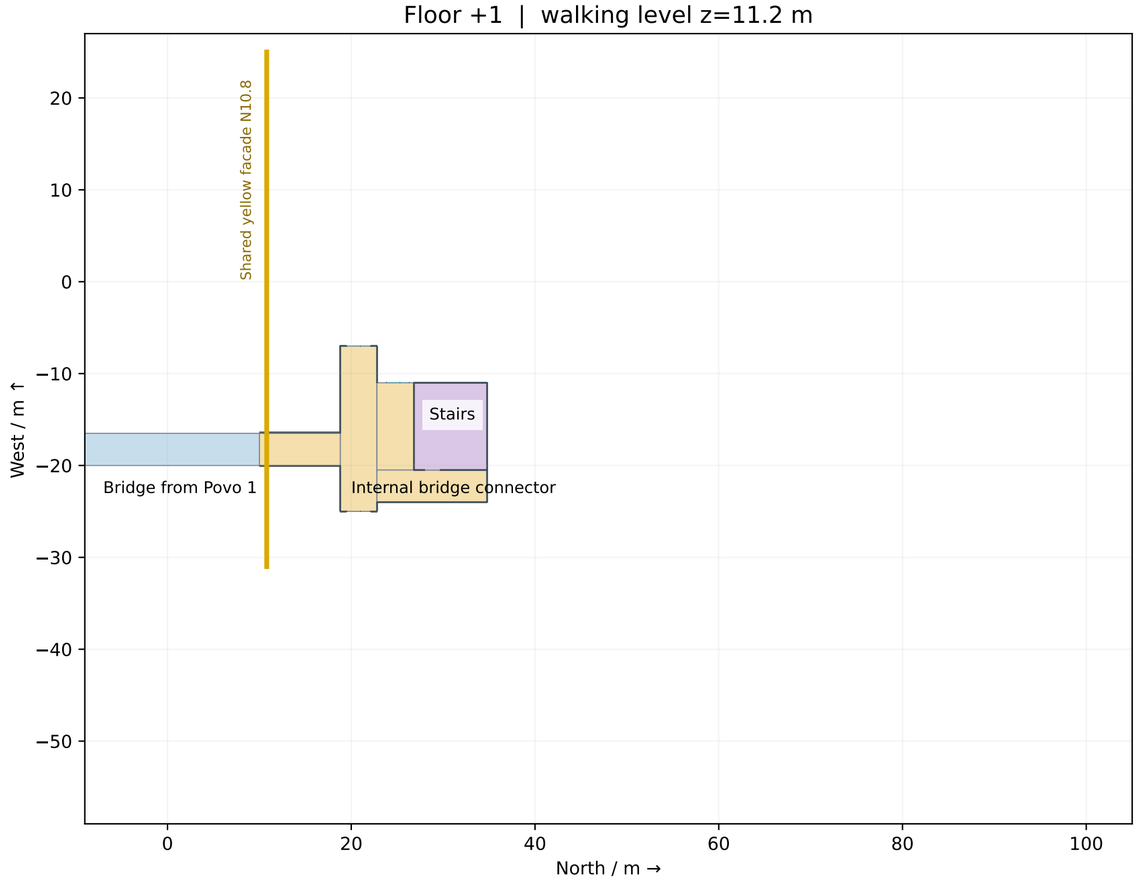

All panels: identical orientation and scale. Enter from bottom; stairwell is left of reception. No lift. Walls and treads are actual geometry.
Room colours identify existing model areas; blank space is not a claim about the real building. Fitted estimates, not a metric survey. Native CS2 validation pending.

POVO 2 — IMPLEMENTED EXTERIOR CONNECTION AND LANDSCAPE

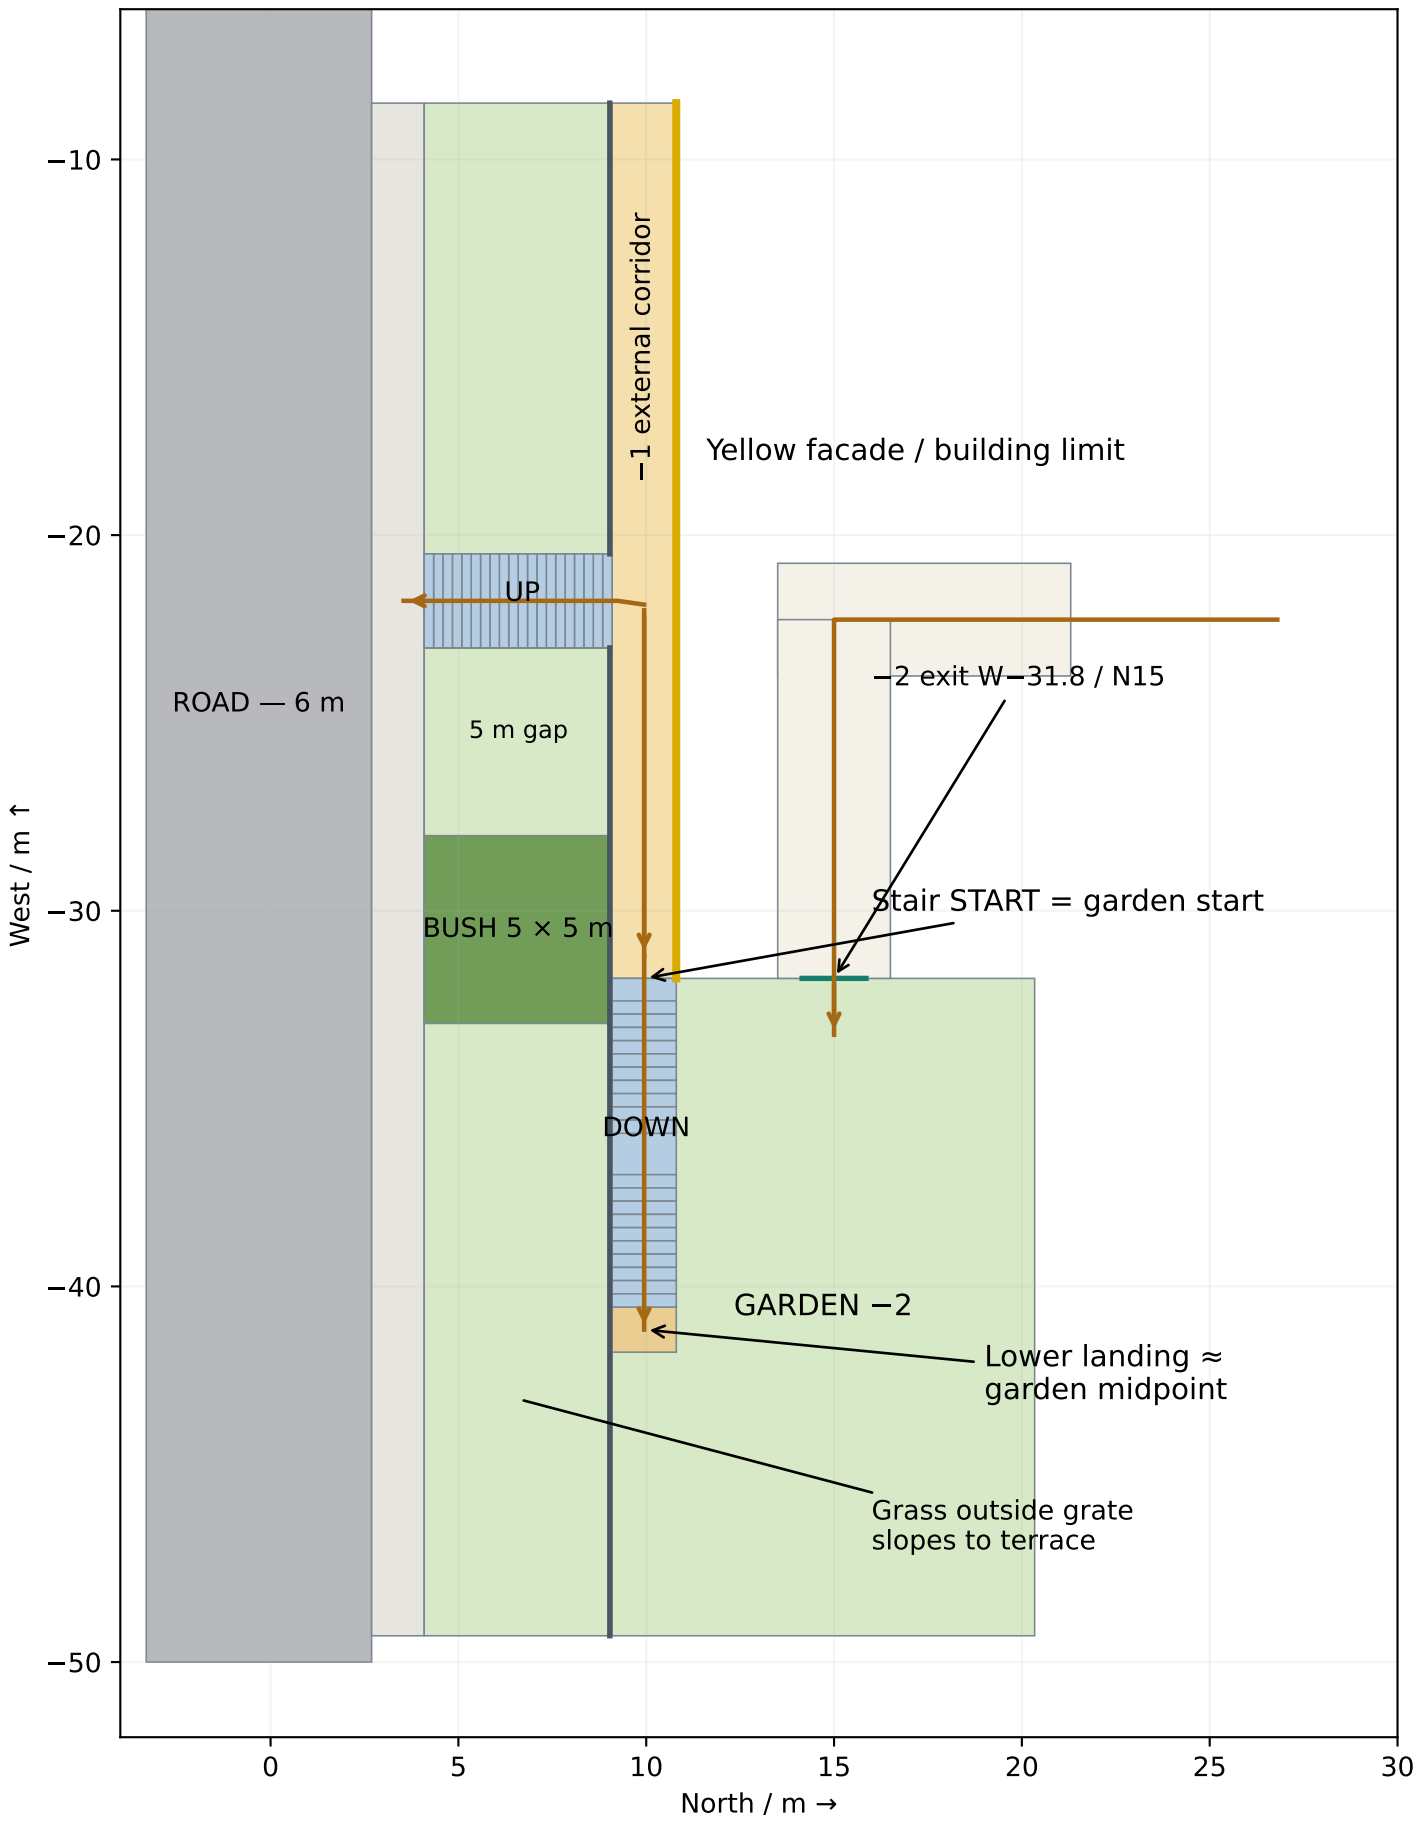

Implemented fitted dimensions
Room depth: 13.4 m
Room corridor: 2.6 m
Terrace width: 1.71 m
Grass width: 5 m
Pavement: 1.4 m
Road: 6 m
Garden: 17.5 × 11.25 m

Bush starts 5 m beyond
UP stair right edge.

DOWN remains eastward,
along wall below road.

External bridge retained

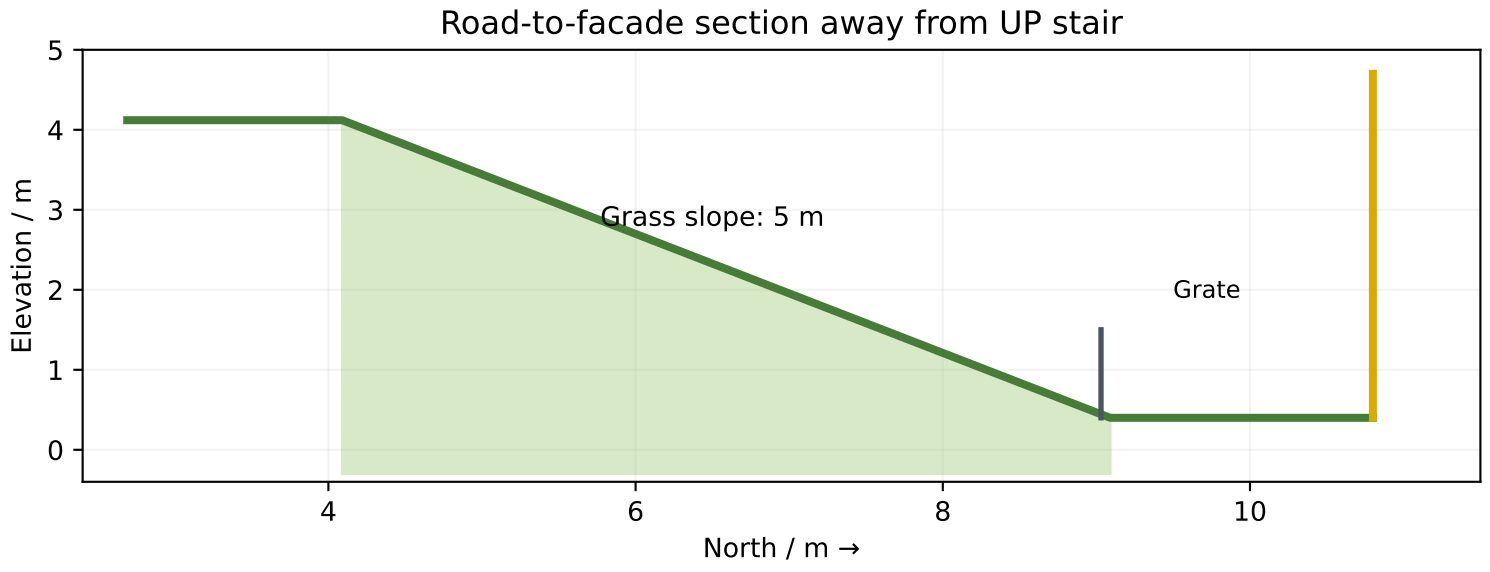

Same orientation as page 1. Plan footprints derive from registered assembly; section uses local road/pavement height at the UP stair.
Topology confirmed by user; dimensions fitted, not surveyed. Final export stage implemented; no native CS2 compilation or in-game validation claimed.